


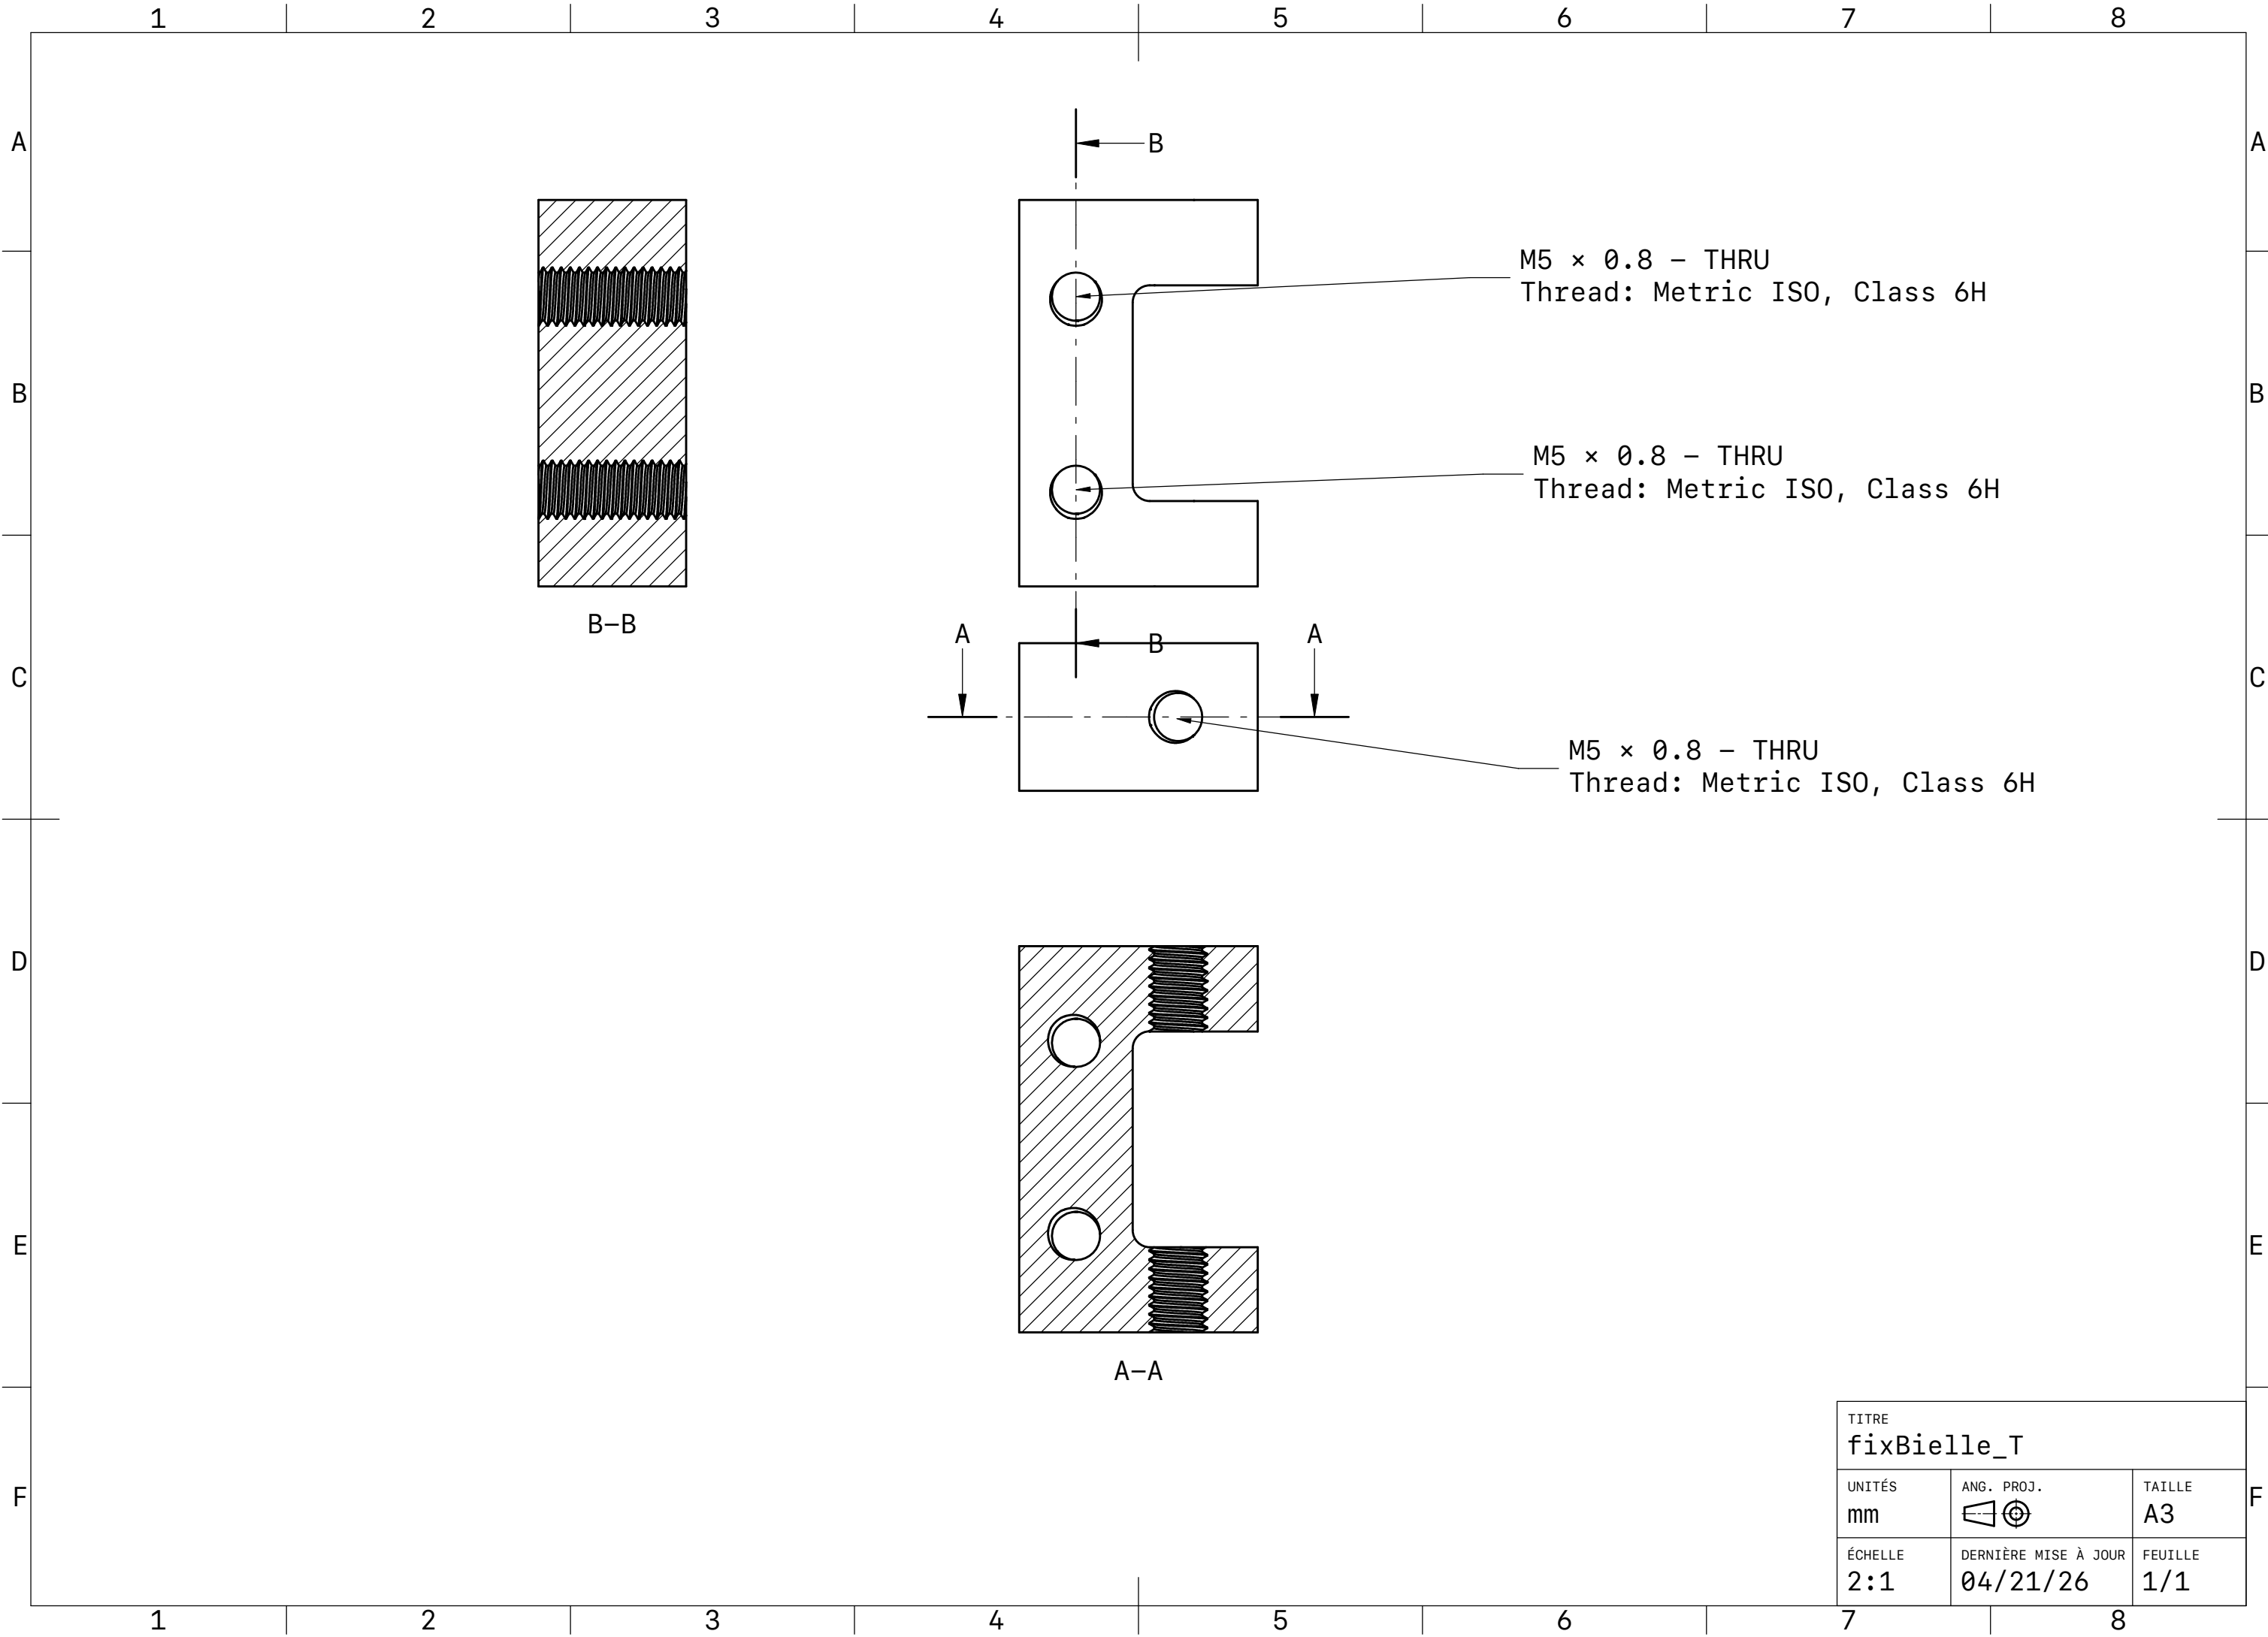

TITRE fixBielle_T		
UNITÉS mm	ANG. PROJ. 	TAILLE A3
ÉCHELLE 2:1	DERNIÈRE MISE À JOUR 04/21/26	FEUILLE 1/1