


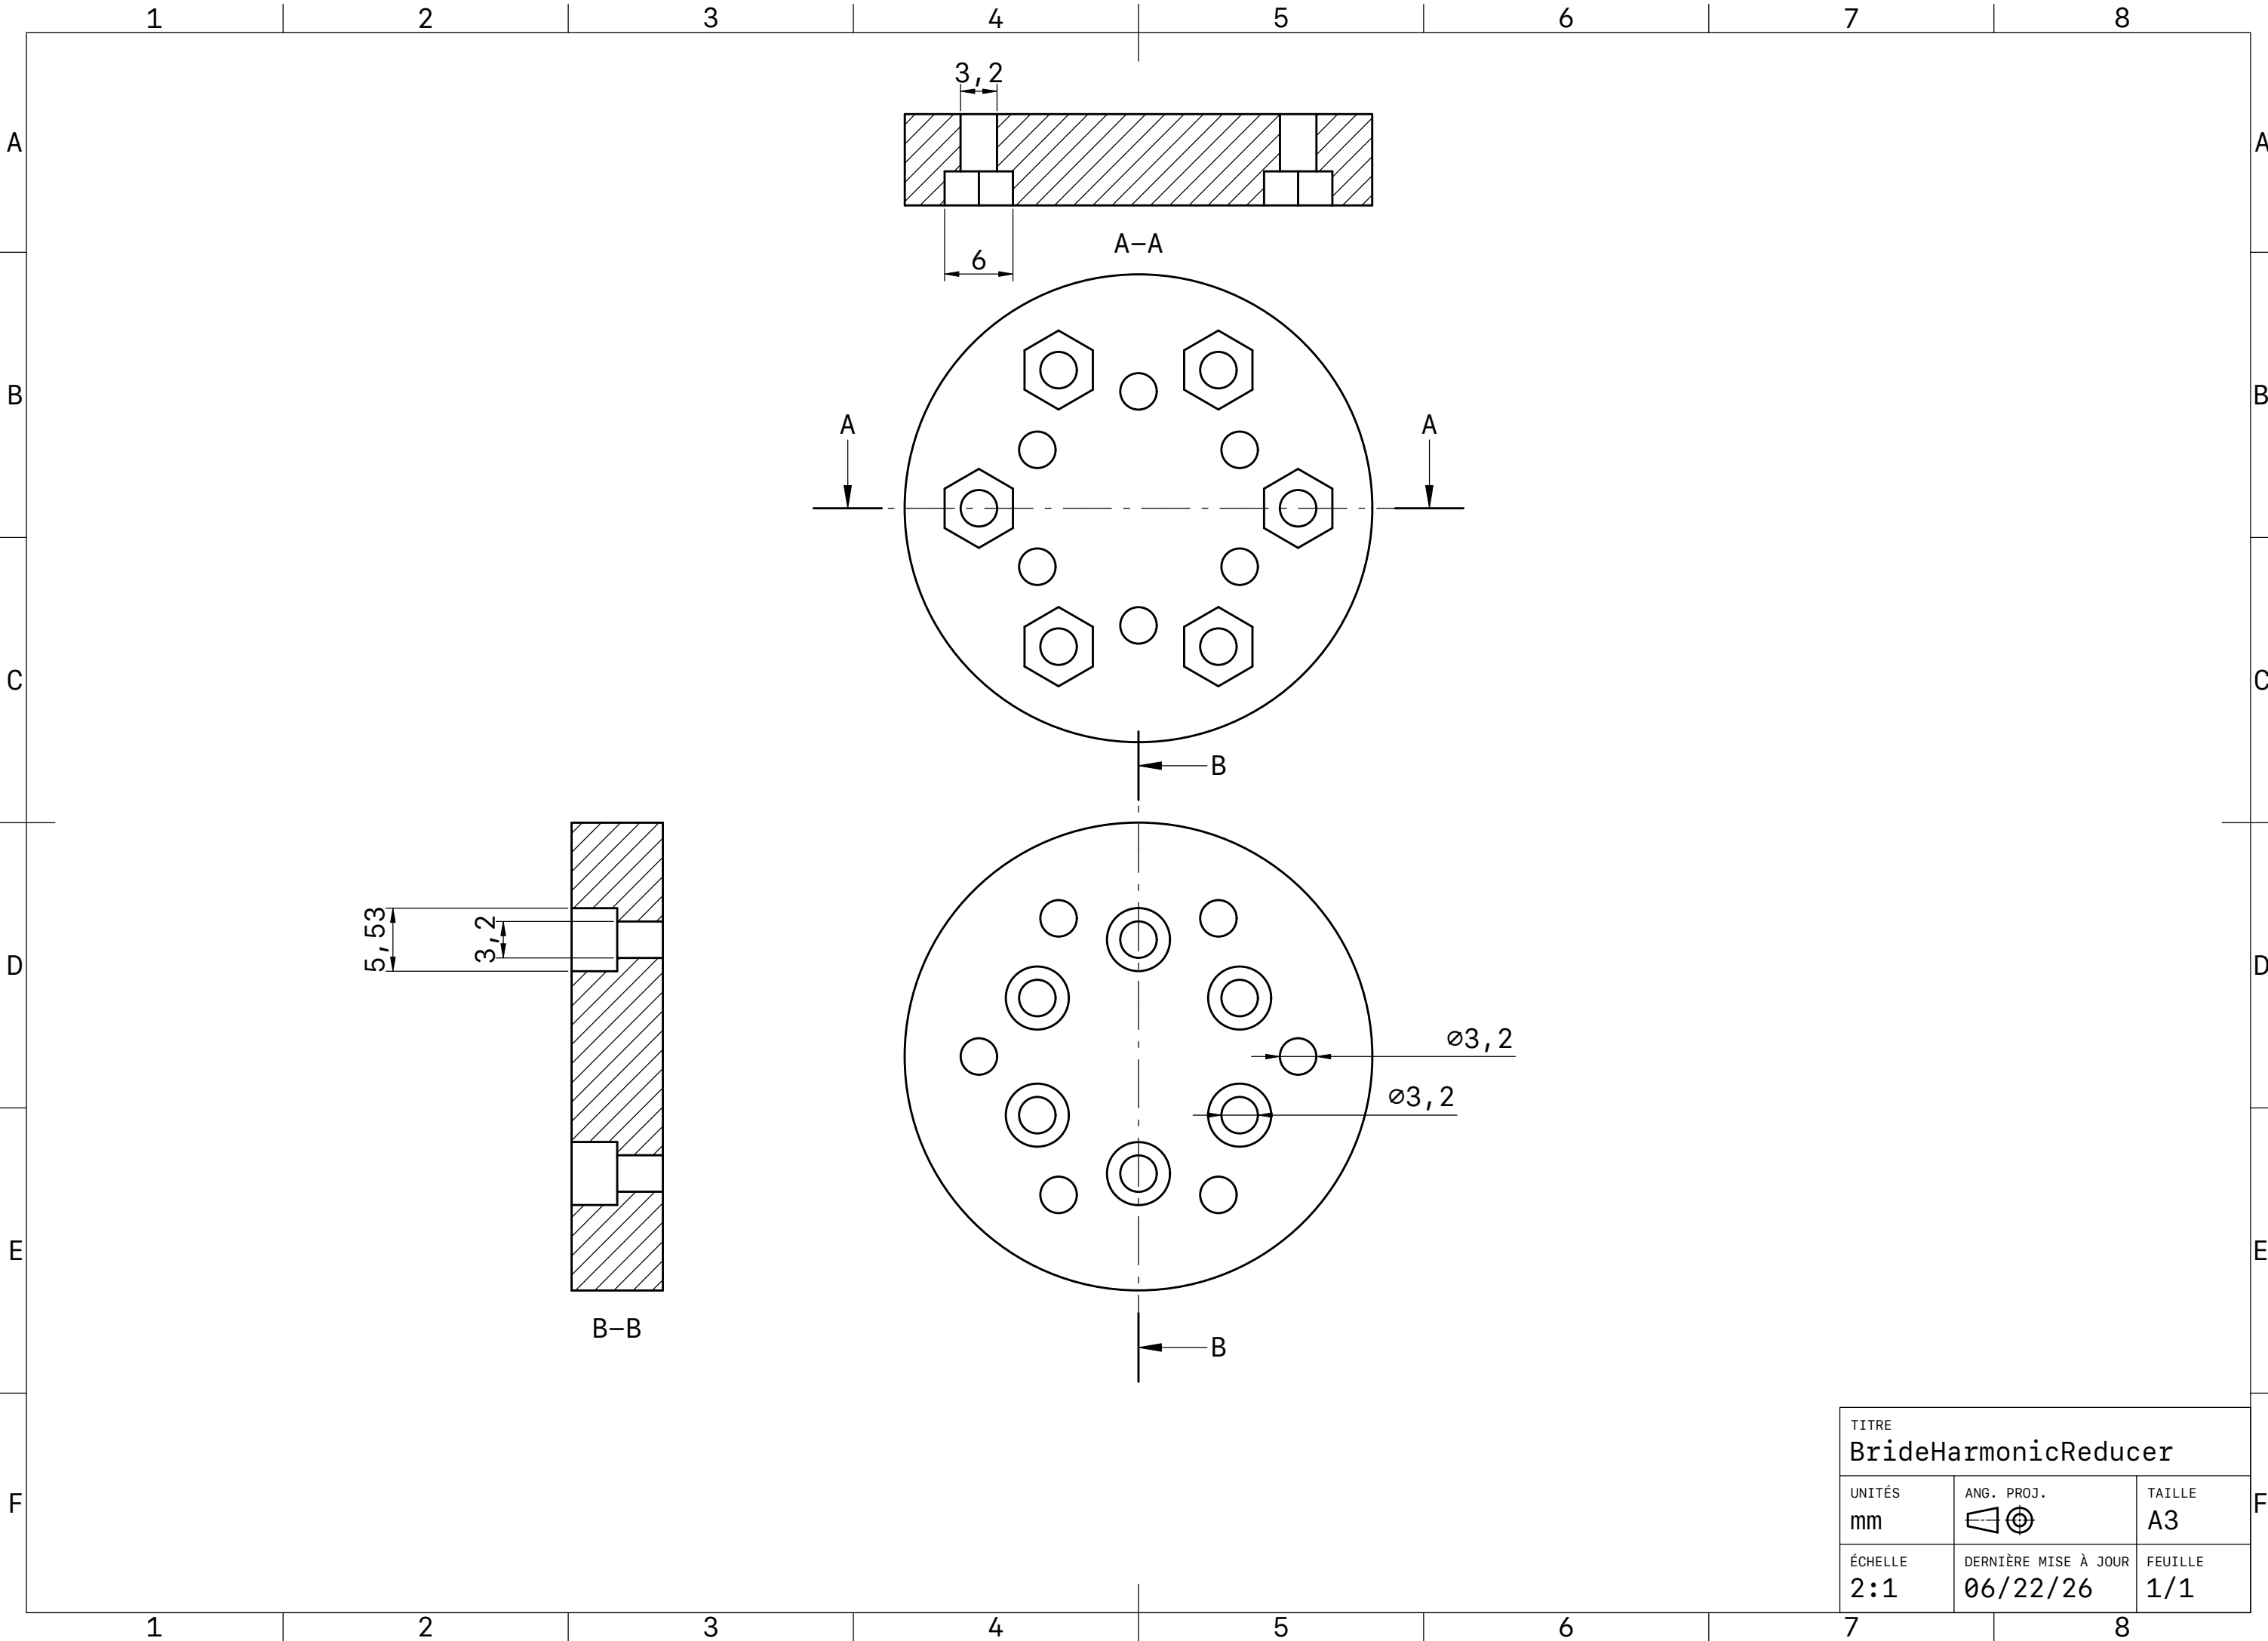

TITRE BrideHarmonicReducer		
UNITÉS mm	ANG. PROJ. 	TAILLE A3
ÉCHELLE 2:1	DERNIÈRE MISE À JOUR 06/22/26	FEUILLE 1/1